

Кому:

В Администрацию
г. Челябинска

От кого:

Митоненкова

Александра

Александровича

(фамилия, имя, отчество)

г. Челябинск

ул. Шенкина 78А


(почтовый адрес для направления ответа)

8-912-770-86-82

(контактный телефон)

Уровнению Федеральной службы государственной
регистрации кадастра и картографии по Челябинской об.
от 23.08.2023 N КУВД-001/2023-21101558 на мой адрес
выдано уведомление об устранении реестровой ошибки
о местоположении границ земельного участка
с кадастровым номером 74:36:0204015:21 расположенного:
г. Челябинск, ул. Шенкина земельный участок 78А

Согласно представленной схеме границ земельных
участков, между участками 21, 22, 25 и участком
безхозяйный земельный участок.

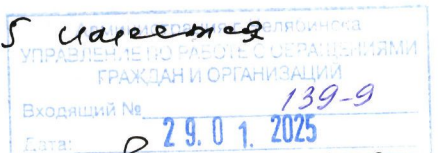

Убедительно прошу Вас рассмотреть вопрос купле
продажи земельного участка прилегающего к
границам моего земельного участка с кадастровым
номером 74:36:0204015:21. Схема с координатами представлена.
Границы земельного участка и доля небавытые
в отношении их окружающих зем. участков.

В свою очередь хочу сообщить Вам, что
акладочное письмо, я писал в 2023 году
и оно поступило из администрации в
земельный кабинет 13.10.23 года
входящий номер 40-171 Подовой Анне
Сергеевне тел. 264-66-48.

ответа я не получил.

Прошу все рассмотреть данный вопрос
и пожалуйста решить положительно.

Если потребуется могу легко объяснить
более подробно образование безхозного
земельного участка который я хочу купить.

28 января 2025г. С уважением 

Управление Федеральной службы
государственной регистрации, кадастра и
картографии по Челябинской области
(Челябинский отдел)
454048, г. Челябинск, ул. Елькина, 85
телефон: (8351) 237-67-45, факс 260-34-40,
74_upr@rosreestr.ru

Антонников Михаил Александрович
Россия, Челябинская обл., г. Челябинск, ул.
Шишкина, дом №78-А

Дата 23.08.2023 № КУВД-001/2023-21101558

**Уведомление об устранении реестровой ошибки в сведениях Единого
государственного реестра недвижимости о местоположении границ земельного
участка в соответствии с частью 7 статьи 61 Федерального закона от 13 июля 2015 г.
№ 218-ФЗ "О государственной регистрации недвижимости"**

В соответствии с ч.8 ст. 61 Федерального закона от 13.07.2015 № 218-ФЗ «О государственной регистрации недвижимости» (далее – Закон о регистрации) уведомляем Вас об исправлении 23 августа 2023 г. органом регистрации прав реестровой ошибки в сведениях Единого государственного реестра недвижимости (ЕГРН) о местоположении границ земельного участка с кадастровым номером 74:36:0204015:21, расположенного: Российская Федерация, Челябинская область, городской округ Челябинский, внутригородской район Тракторозаводский, город Челябинск, улица Шишкина, земельный участок 78А.

Сведения о результатах исправления реестровой ошибки:

Обозначение характерных точек границ	Значения координат, м				Значения площади, м2	
	до исправления реестровой ошибки		после исправления реестровой ошибки		до исправления реестровой ошибки	после исправления реестровой ошибки
	X	Y	X	Y		
1	2	3	4	5	6	7
1	2328522.0 3	608590.01	2328522.0 3	608590.01	339	339
2	2328540.4 6	608588.9	2328540.4 6	608588.9	339	339
3	2328538.0 6	608572.98	2328538.5 1	608572.72	339	339
4	2328529.2 4	608574.12	2328531.0 4	608573.61	339	339
5	2328528.8 8	608570.14	2328530.7 7	608571.33	339	339
6	2328517.4	608572.83	2328528.8 7	608571.47	339	339
7	-	-	2328517.4	608572.83	339	339
8	-	-	2328520.5	608584.31	339	339
9	-	-	2328521.3 3	608587.41	339	339
1	2328522.0 3	608590.01	2328522.0 3	608590.01	339	339

Государственный регистратор прав



Подпись, М.П.)

Конашева И.В.
(фамилия, инициалы)

Тел. 237-27-62
261-89-53



Схема границ земельных участков, границ (частей границ) муниципальных образований, населенных пунктов, территориальных зон, лесничеств, в описании местоположения которых выявлена реестровая ошибка

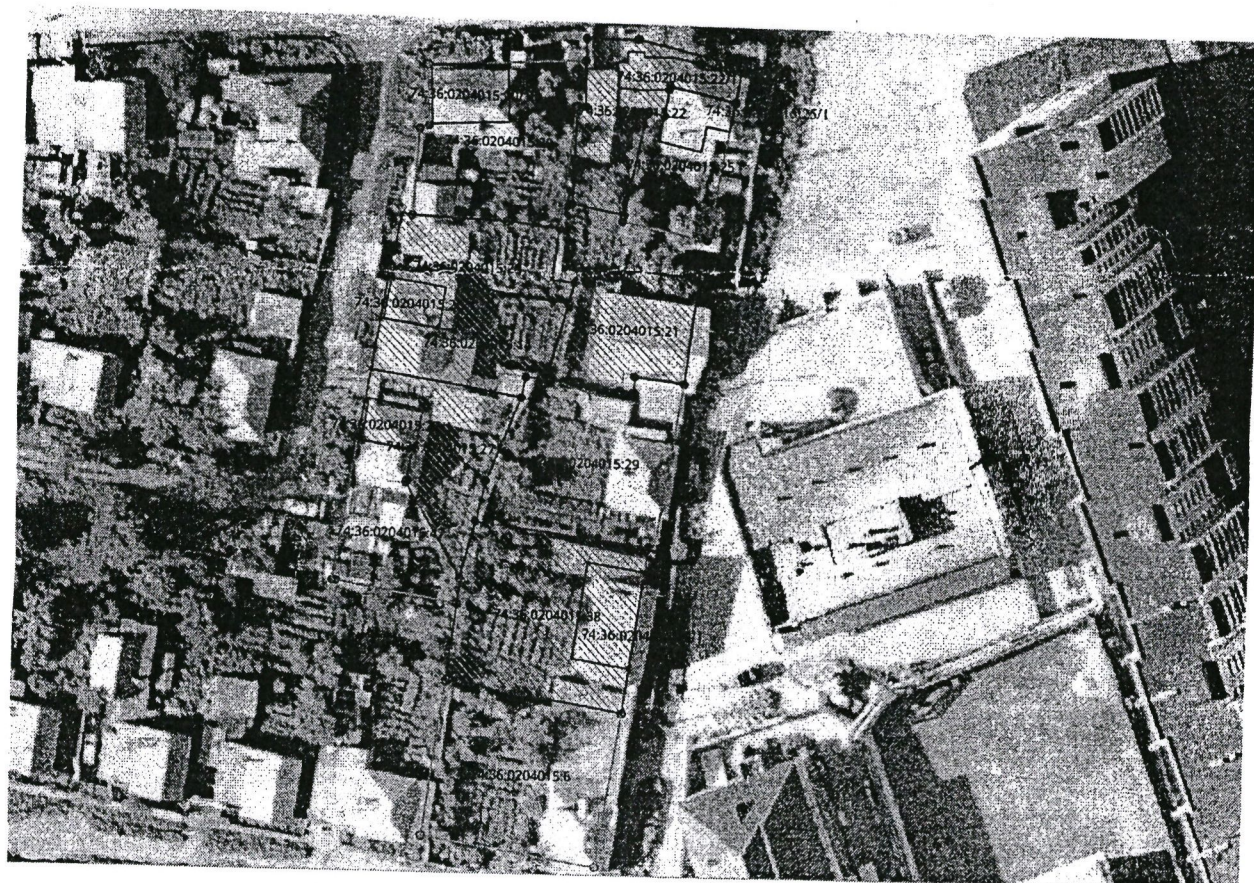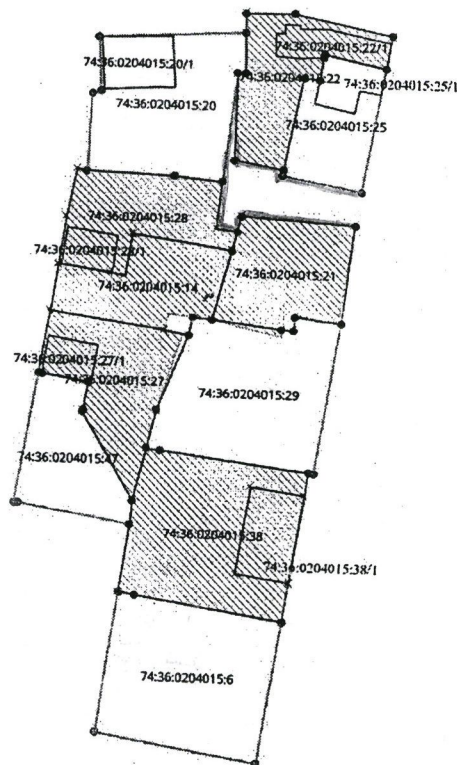

Утверждена

(наименование документа об утверждении, включая

наименования органов государственной власти или

органов местного самоуправления, принявших

решение об утверждении схемы или подписавших

соглашение о перераспределении земельных участков)

от

№

Схема расположения земельного участка или земельных участков на кадастровом плане территории

Условный номер земельного участка 74:36:0204015:3У1		
(указывается в случае, если предусматривается образование двух и более земельных участков)		
Площадь земельного участка 506 м ²		
(указывается проектная площадь образуемого земельного участка, вычисленная с использованием технологических и программных средств, в том числе размещенных на официальном сайте федерального органа исполнительной власти, уполномоченного Правительством Российской Федерации на осуществление государственного кадастрового учета, государственной регистрации прав, ведение Единого государственного реестра недвижимости и предоставление сведений, содержащихся в Едином государственном реестре недвижимости, в информационно-телекоммуникационной сети "Интернет" (далее - официальный сайт), с округлением до 1 квадратного метра. Указанное значение площади земельного участка может быть уточнено при проведении кадастровых работ не более чем на десять процентов)		
Обозначение характерных точек границ	Координаты, м	
	(указываются в случае подготовки схемы расположения земельного участка с использованием технологических и программных средств, в том числе размещенных на официальном сайте. Значения координат, полученные с использованием указанных технологических и программных средств, указываются с округлением до 0,01 метра)	
	X	Y
1	2	3
1	608572,83	2328517,40
2	608584,31	2328520,50
3	608587,41	2328521,33
4	608587,85	2328517,87
5	608595,59	2328518,82
6	608598,61	2328519,18
7	608596,88	2328528,49
8	608594,47	2328541,45
9	608588,90	2328540,46
10	608572,72	2328538,51
11	608573,61	2328531,04
12	608571,33	2328530,77
13	608571,47	2328528,87
1	608572,83	2328517,40



Система координат: МСК-74, зона 2
Масштаб 1:500

Условные обозначения:


- — граница образуемого земельного участка,
- — граница учтенного земельного участка,
- - - — граница кадастрового квартала,
- — характерная точка границы земельного участка.

74:36:0204015:28

74:36:0204015:14

74:36:0204015:21

5,66

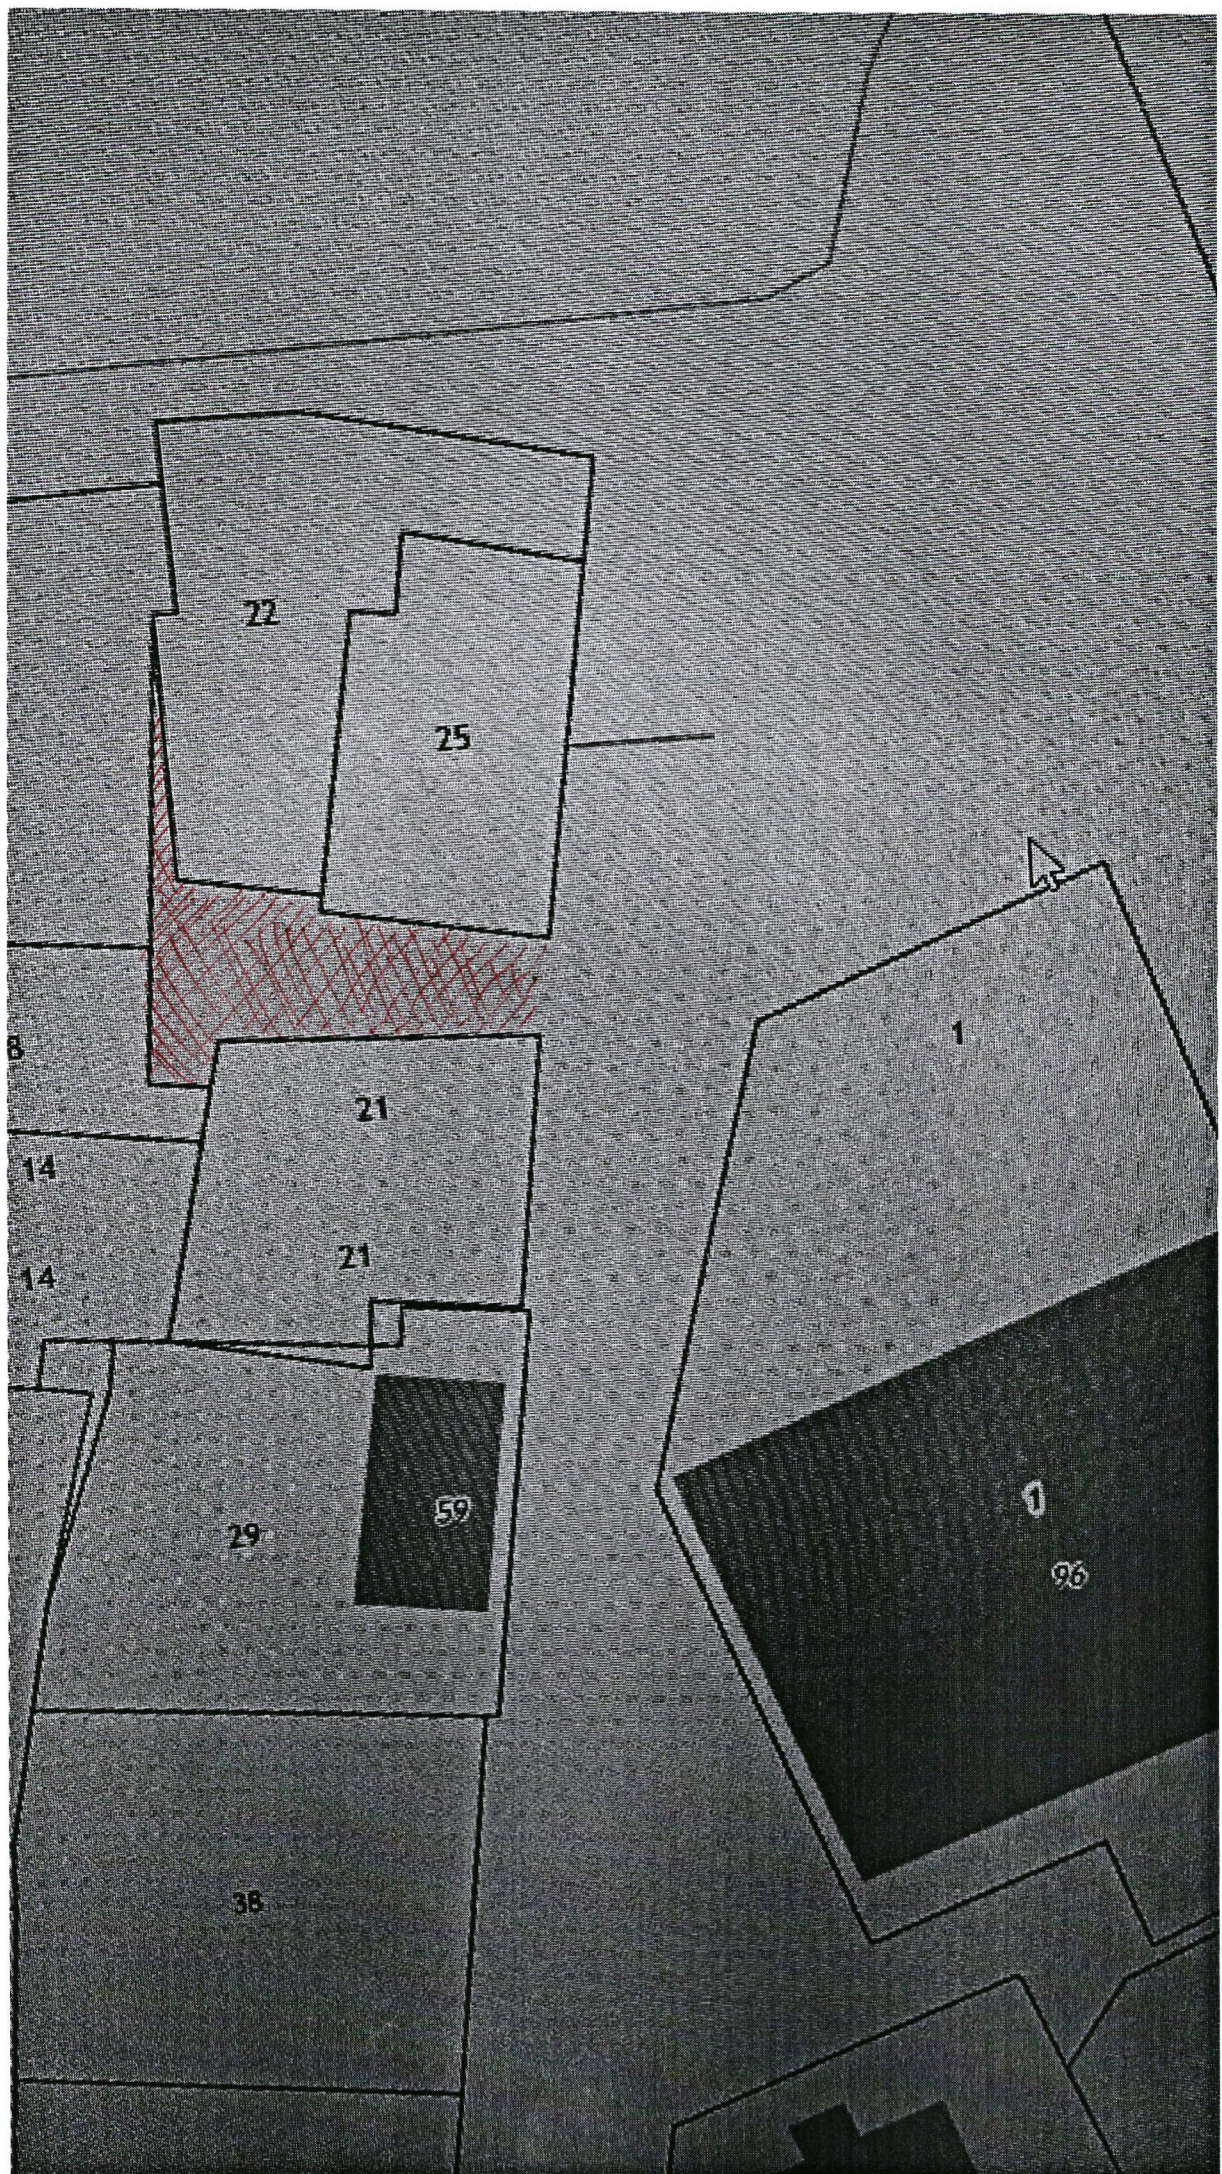

ЭКСПЛИКАЦИЯ:

1-жилой дом

2-баня

Глубина промерзания грунта 190 см.

границы земельного участка
на праве собственности

измененные границы участка

